


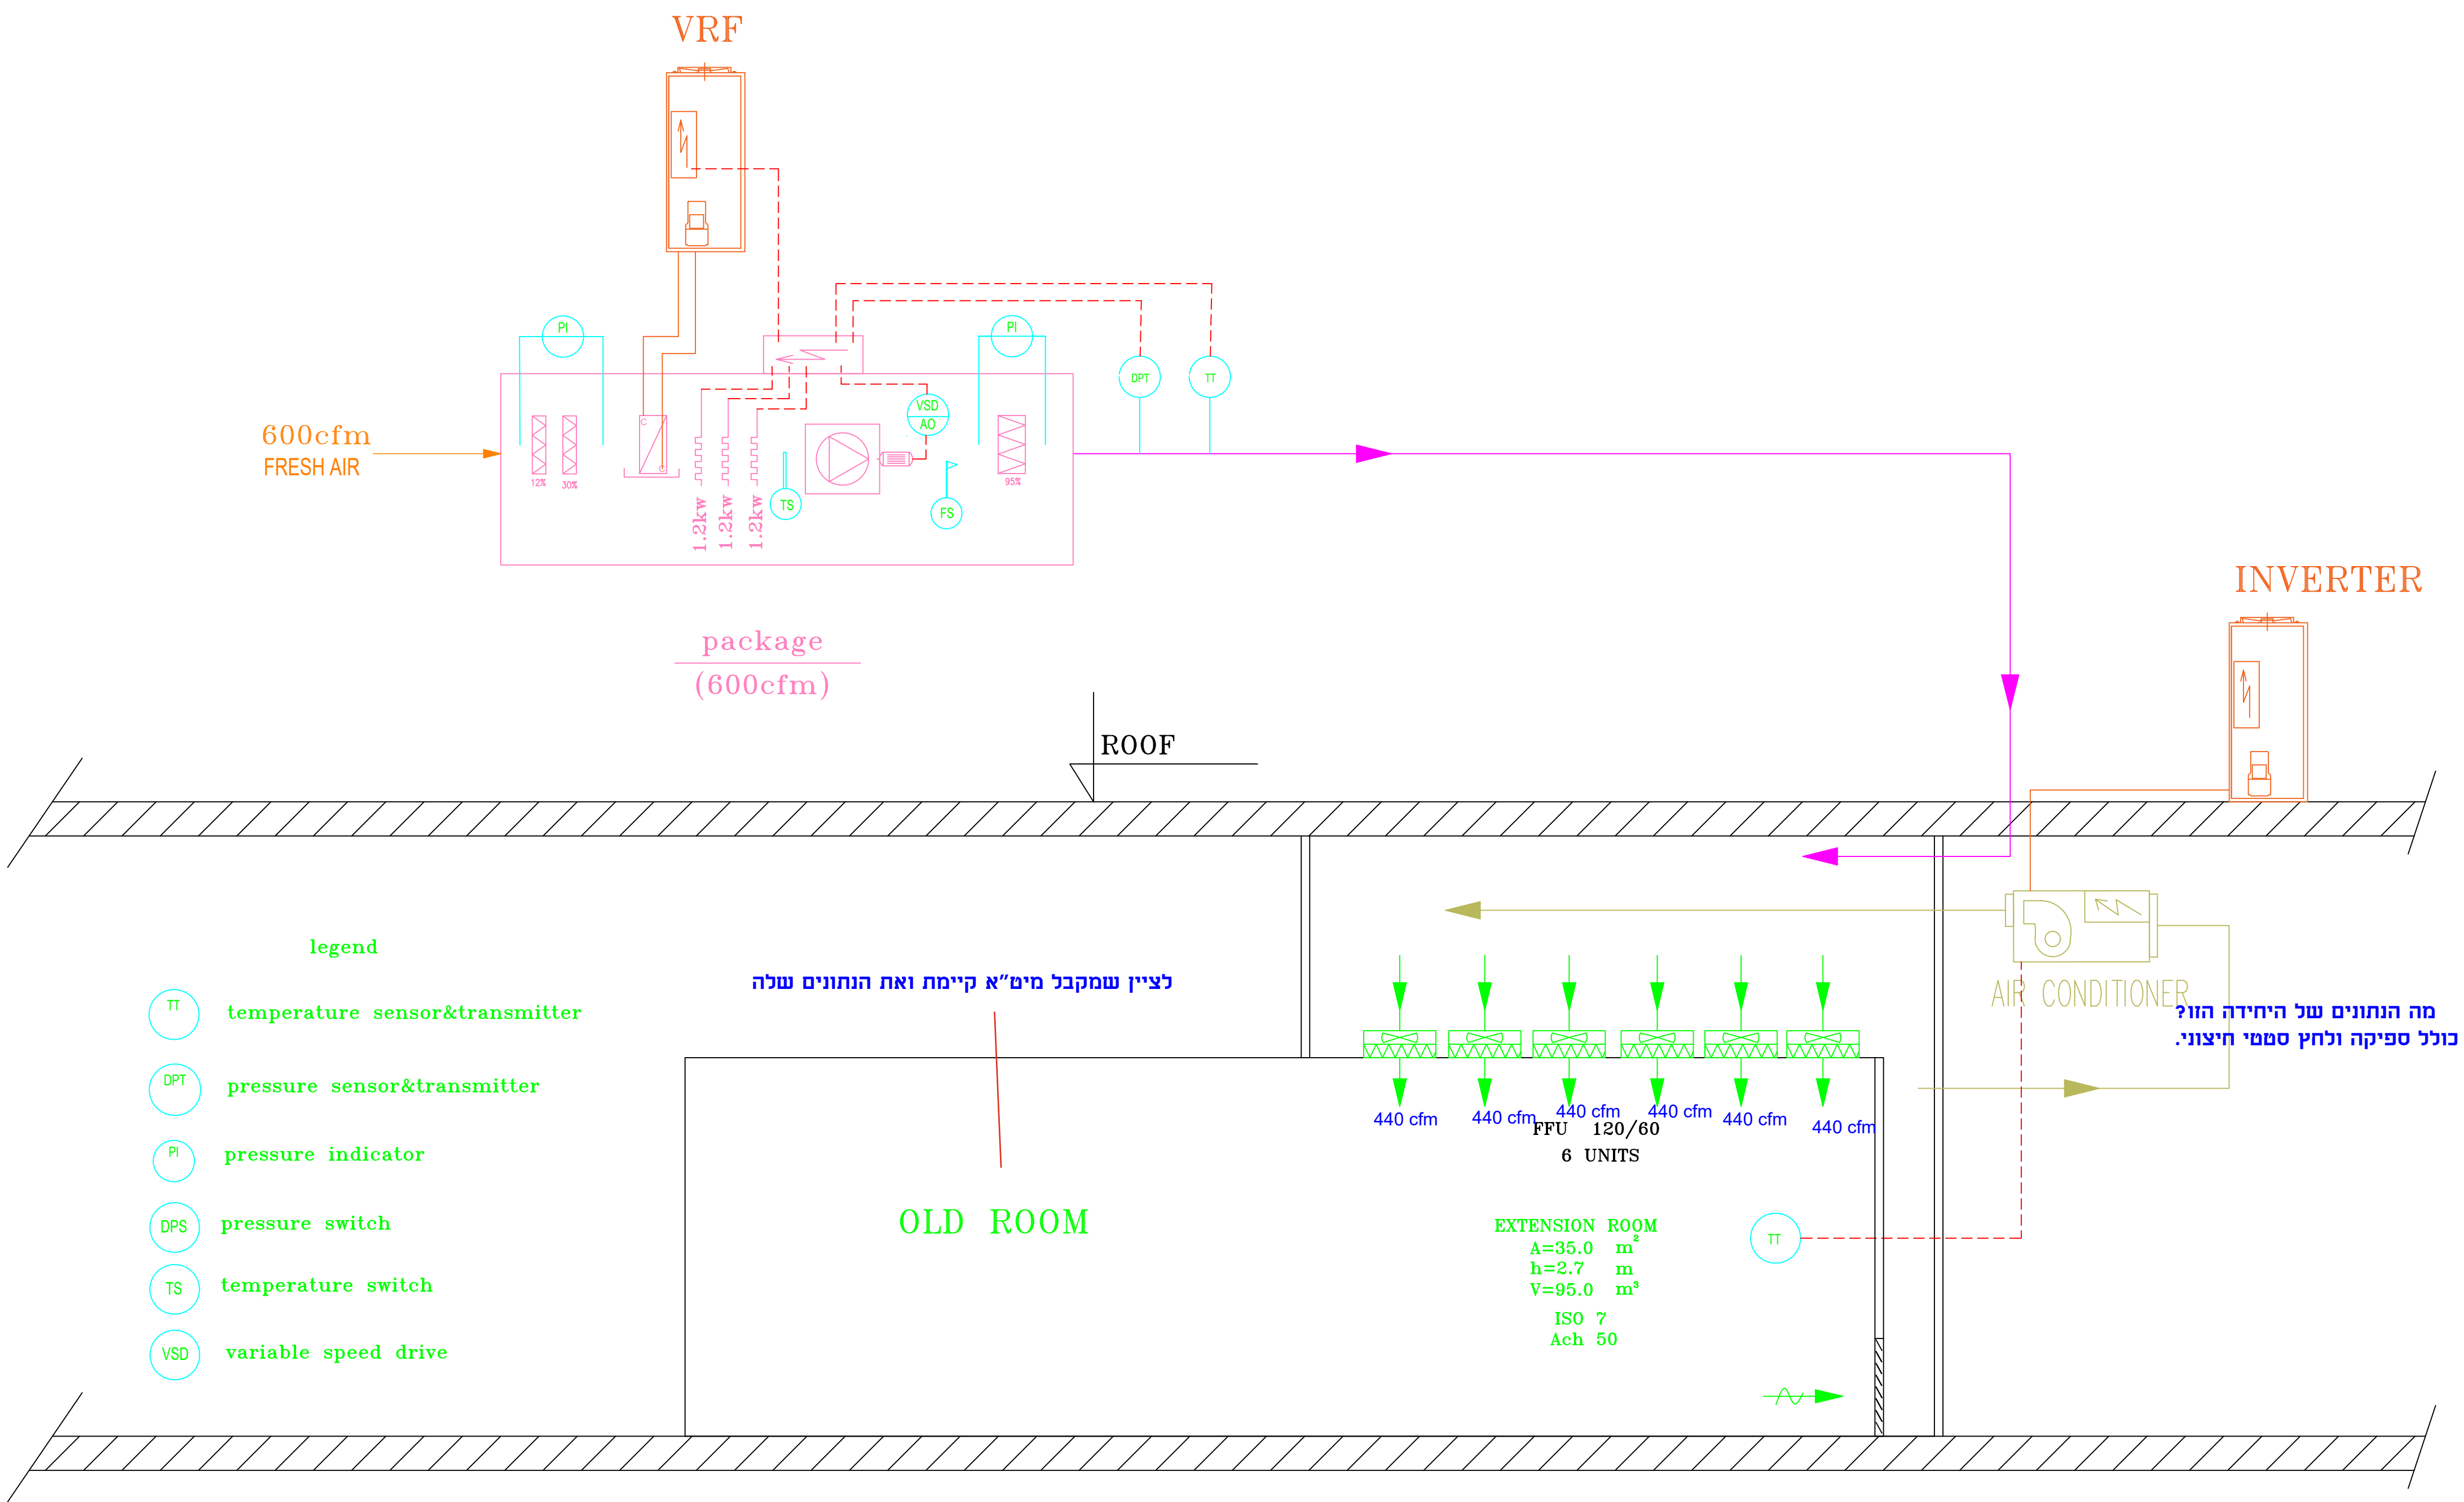

REV	DATE	DESCRIPTION	BY.	nanomotion			
02	7.5.26	add humidifier		DOCUMENT TITLE			
				CLEANROOM HVAC-P&ID		SCALE	
				DOCUMENT NO.		REV.	
				26000017-HVAC-W		00	
				Date: 29.6.26			

STATUS	DATE	DESIGNED	CHECKED
COMMENTS		BY Yehezkel	BY Yehezkel
APPROVAL		DATE 29.6.26	DATE 29.6.26
CONSTRUCTION		DRAWN	APPROVED
AS MADE		BY Yehezkel	BY Yehezkel
other		DATE 29.6.26	DATE 29.6.26

A.D. CLEAN ROOMS

KATZGROUP

E-MAIL INFO@CLEANROOMS.CO.IL

WEB SITE WWW.CLEANROOMS.CO.IL

כרמיאל היוצרים 22

טלפון: 04-8332298

פקס: 04-8332293

CARMIEL HAYOZRIM 22

TEL: 972-4-8332298

FAX: 972-4-8332293

דואר אלקטרוני

אתר אינטרנט